

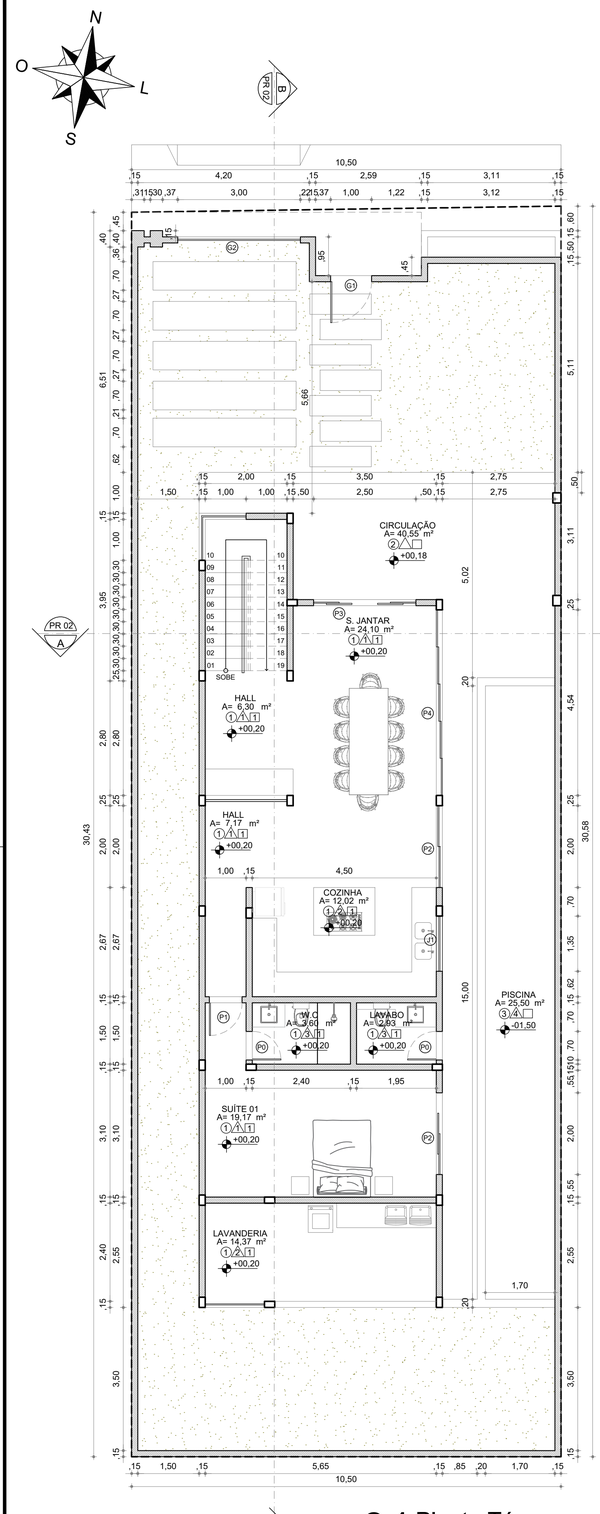



01 Planta Térreo
Escala 1:75

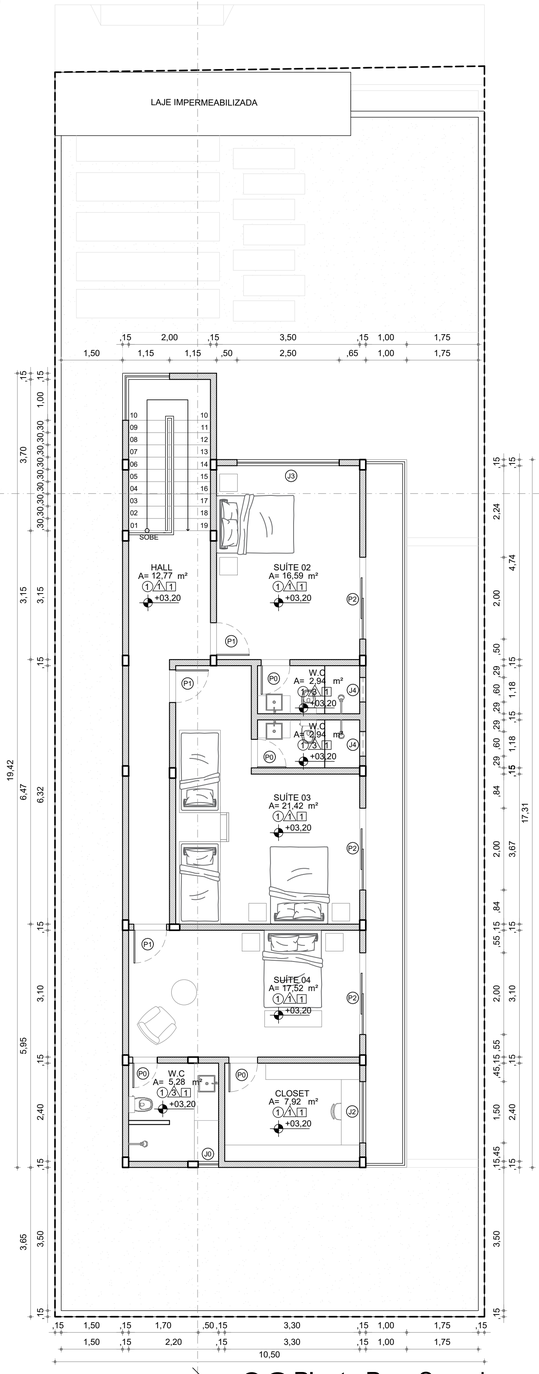

02 Planta Pav. Superior
Escala 1:75

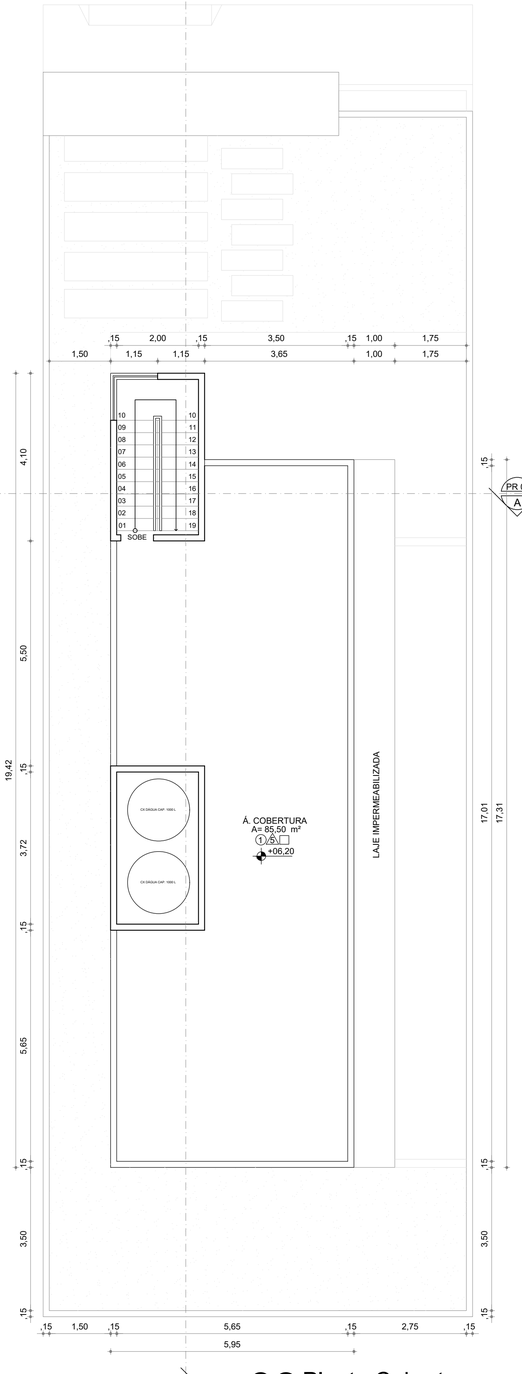

03 Planta Cobertura
Escala 1:75

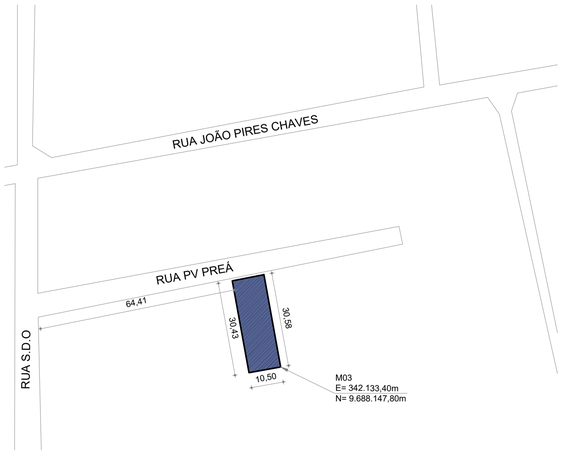

04 Planta Situação
Escala 1:1000

QUADRO DE ESQUADRIAS

CÓDIGO	LARG (m)	ALT (m)	PEIT (m)	TIPO	QTD	DESCRIÇÃO
PORTAS						
P0	0.70	2.10	---	ABRIR	06	PORTA EM MADEIRA MACIÇA PINTADA NA COR BRANCA
P1	0.80	2.10	---	ABRIR	04	
P2	2.00	2.40	---	CORRER	05	PORTA DE VIDRO ESTRUTURADA EM METALON PINTADA NA COR CHUMBO - 02 FOLHAS
P3	2.50	2.40	---	CORRER	01	
P4	4.54	2.40	---	CORRER	01	PORTA DE VIDRO ESTRUTURADA EM METALON PINTADA NA COR CHUMBO - 04 FOLHAS
JANELAS						
J0	0.50	1.50	0.60	GUILHOTINA	01	JANELA EM VIDRO 6mm TRANSPARENTE E PERFIL EM METALON NA COR CHUMBO
J1	1.35	1.40	1.00	CORRER	01	
J2	1.50	1.40	1.00	CORRER	01	
J3	2.50	1.40	1.00	CORRER	01	
J4	0.60	0.60	1.80	BASCULANTE	02	JANELA EM VIDRO 6mm TRANSPARENTE E PERFIL EM METALON NA COR CHUMBO COM SIST. DE REG. INTERNO
PORTÃO						
G1	1.00	2.10	---	ABRIR	01	PORTÃO EM METALON NA COR CHUMBO
G2	3.00	2.10	---	CORRER	01	PORTÃO EM METALON NA COR CHUMBO

QUADROS DE ÁREAS

ÁREA CONSTRUÍDA TÉRREO	A= 107,84m²
ÁREA CONSTRUÍDA PISCINA	A= 25,50m²
ÁREA CONSTRUÍDA PAV. SUPERIOR	A= 125,15m²
ÁREA CONSTRUÍDA TOTAL	A= 258,49m²
ÁREA COBERTA TOTAL	A= 125,15m²
ÁREA TERRENO	A= 320,30m²
ÁREA OCUPADA (PROJEÇÃO HORIZONTAL)	A= 150,65m²

INDICADORES DE USO DO SOLO (ZUT II)

	EXIGIDO	PROPOSTO
TAXA DE OCUPAÇÃO	70,00%	47,03%
ÍNDICE DE APROVEITAMENTO	1,40	0,81
TAXA DE PERMEABILIDADE	20,00%	31,71%
ALTURA MÁXIMA	7,50 m	7,50 m
RECUOS FRONTAL E DE FUNDOS	3,00 m E 3,00 m	5,66 m E 3,50 m
RECUOS LATERAIS	1,50 m E 0,00m	1,50 m E 0,00 m

REVISÃO	DESCRIÇÃO	DESENHO	DATA

archvalle Arquitetura e Construção
(88)99601-8042 | (88)99666-1132
#archvallearquitetura@gmail.com

CÓD. ATIVIDADE	INSCRIÇÃO M.	PESSOA F/J
41.20-4-00	9782	JURÍDICA

CNPJ: 34.929.854/0001-79
FIRMA: Archvalle Arquitetura e Construção LTDA.
LOCAL: Rua 07 de Setembro, 532A, Centro
CEP: 62.560-000, Marco - Ceará

PROJETO: SOBRADO L | R
ARQUITETURA

JUAN NEVES AMÂNCIO
ARQUITETO E URBANISTA
CAU+CE A151920-4
RESPONSÁVEL TÉCNICO

PROPRIETÁRIO(A) OU REPRESENTANTE LEGAL

CLIENTE: LARISSA DE ALBUQUERQUE ROSA
ENDEREÇO: RUA PV PREÁ, SN, VILA PREÁ, CRUZ, CEARÁ

DESENHOS DA PRANCHA:		ESCALA:	PRANCHA:
01	PLANTA TÉRREO	1:75	001 002
02	PLANTA PAV. SUPERIOR	1:75	
03	PLANTA COBERTURA E SITUAÇÃO	INDICADA	

ETAPA: ANTE PROJETO

PROJETISTAS:	CAU/CREA
ARQ. JONATAS BRANDÃO	A151910-7
ARQ. JUAN NEVES	A151920-4

RRT:	DESENHO:	EMISSÃO:	REVISÃO:
SI13078532I00CT001	JUAN	31/08/2023 19:05:46	JUAN

ARQUIVO:AV_Arquitetura_R_Juan_Larissa_EP_Sobrado_Rev01_2023-05-23.dwg